

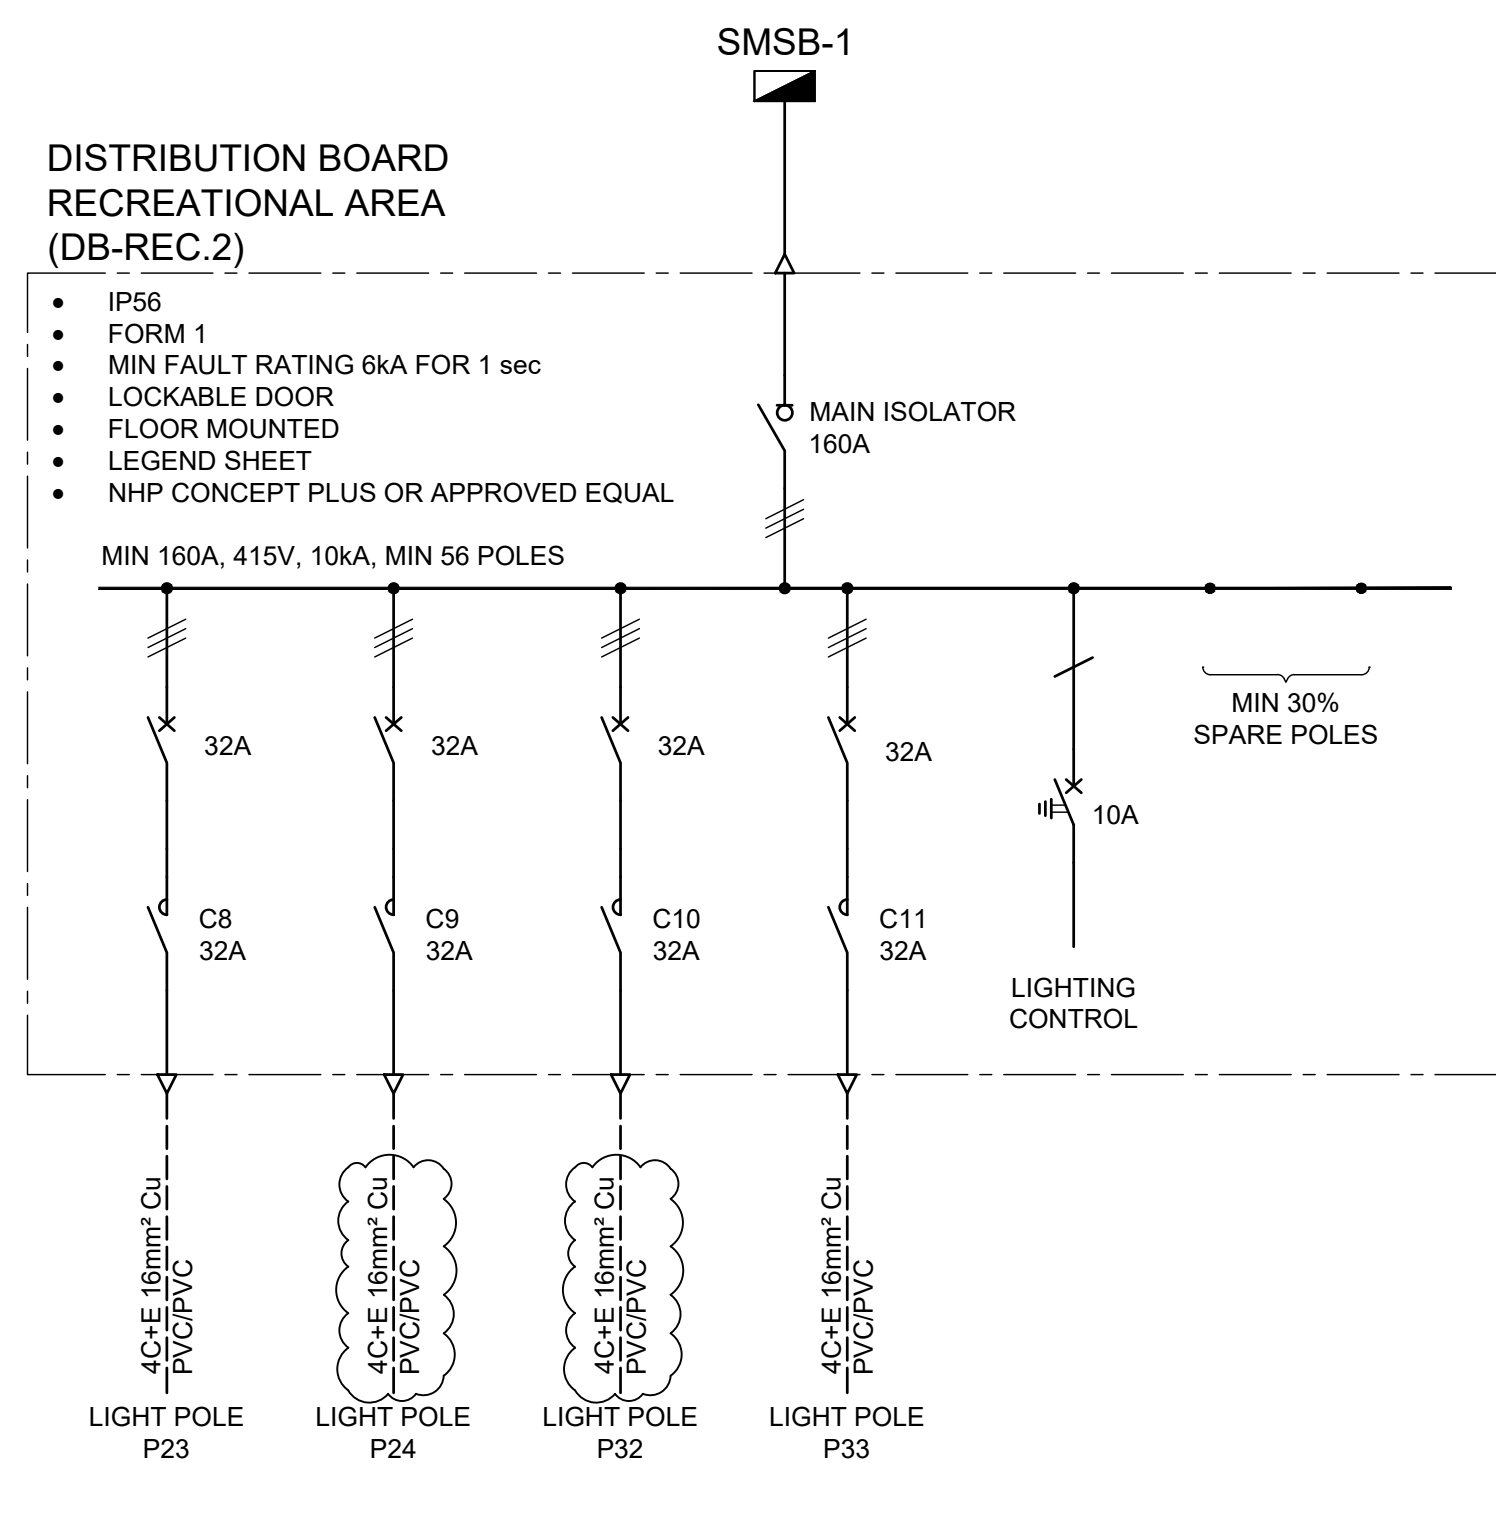
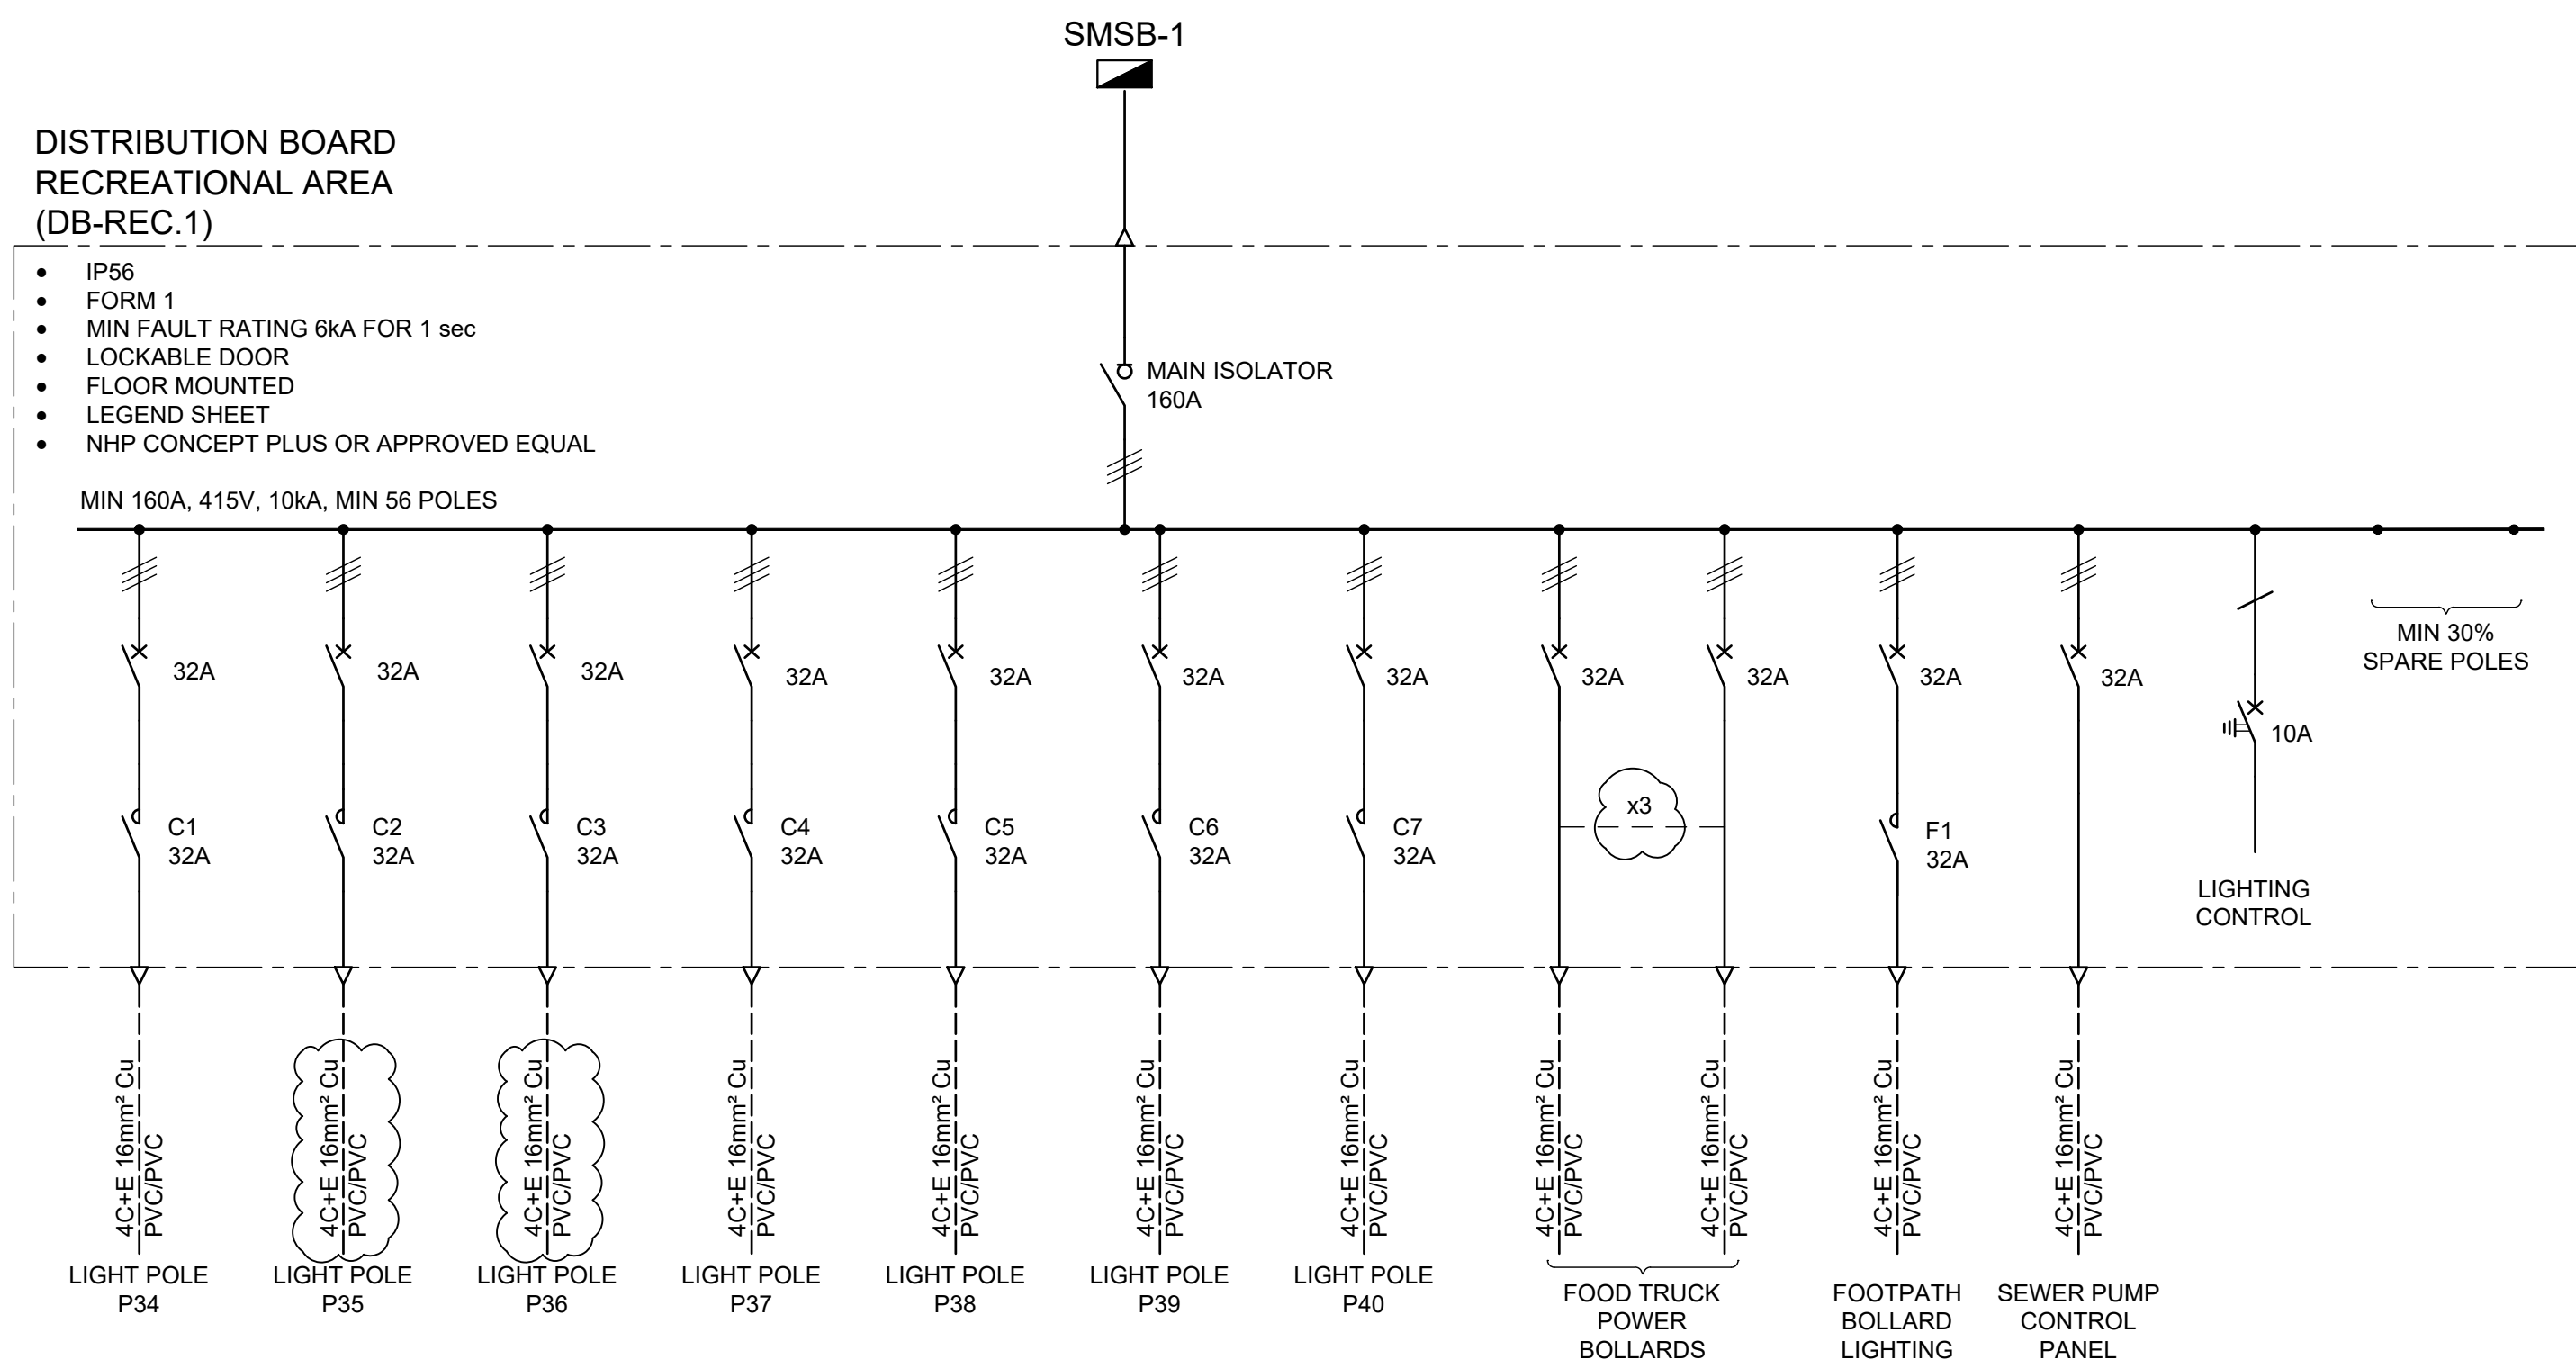


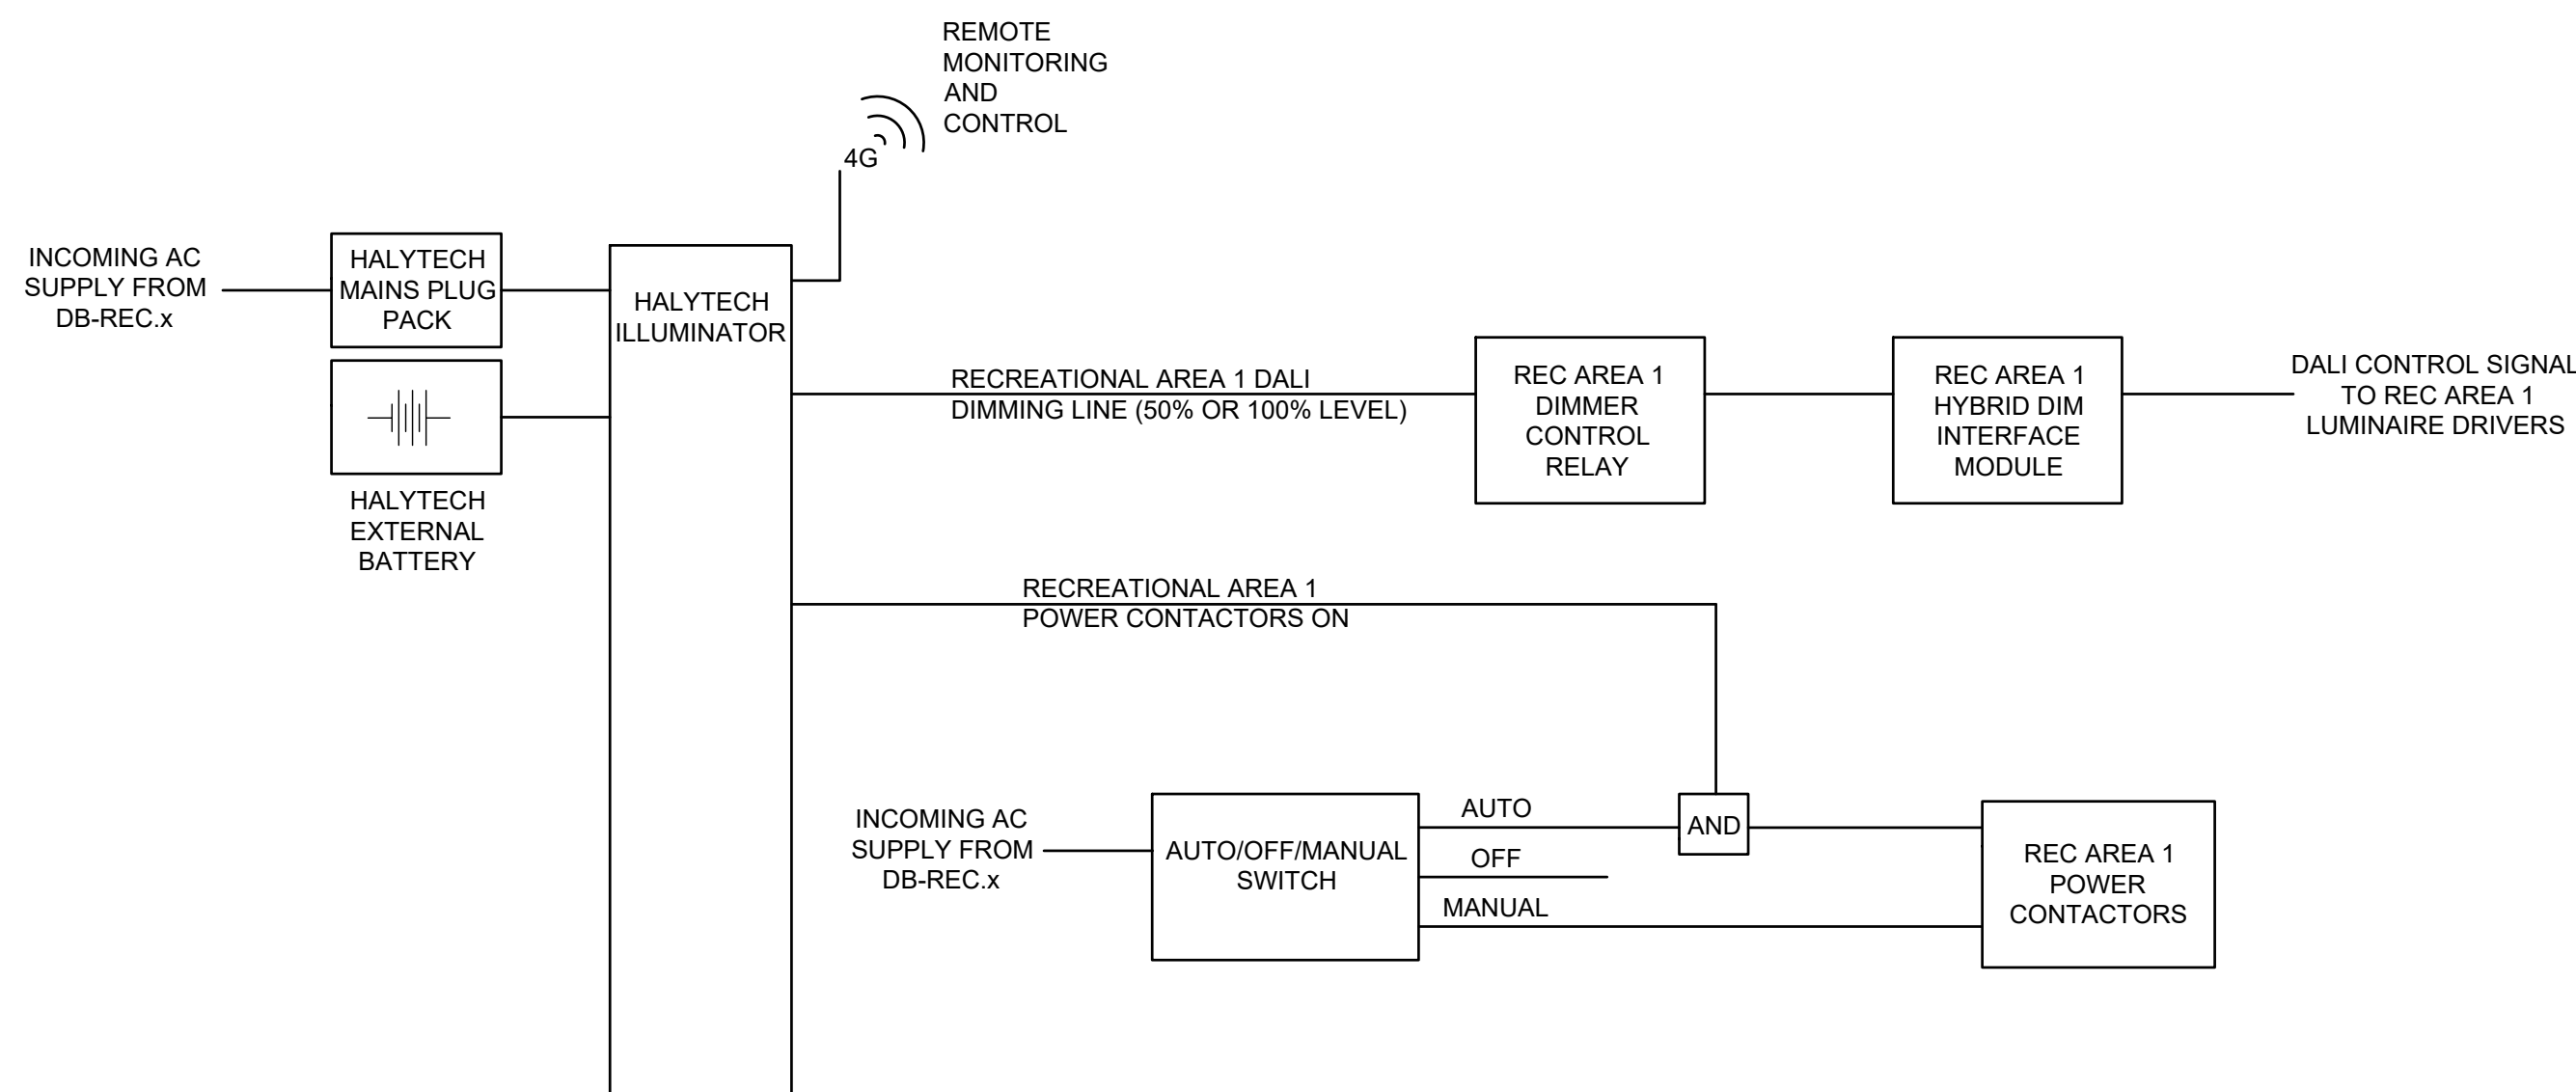

- ### LIGHTING CONTROL NOTES

1. LIGHTING CONTROL TOPOLOGY SHOWN IS FOR LCP-REC 1 FOR REFERENCE. APPLY THE SAME CONTROL STRATEGY FOR LCP-REC 2 AND LCP-REC 3. REFER TO SWITCHING TABLE IN THIS DRAWING.
 2. THE CONTRACTOR SHALL ENGAGE A COMPETENT AND QUALIFIED SUB-CONTRACTOR TO INSTALL THE LIGHTING CONTROL SYSTEM FOR THE EXTERNAL RECREATIONAL AREA.
 3. THE LIGHTING CONTROL IS CONCEPT ONLY. THE CONTRACTOR SHALL SUPPLY AND INSTALL ALL THE NECESSARY EQUIPMENT, CABLING, SWITCHGEAR AND CONTROL GEAR TO MAKE A COMPLETE AND FULLY FUNCTIONAL SYSTEM IN ACCORDANCE WITH THE PERFORMANCE REQUIREMENTS (SEE NOTE 3) AND TO THE APPROVAL OF COUNCIL.
 4. EACH OF THE NETBALL. LIGHTING CONTROL TO BE A HALYTECH CONTROL LIGHTING CONTROL SYSTEM OR EQUIVALENT APPROVED. HOUSED IN A SELF CONTAINED DEDICATED LIGHTING SWITCH PANELS.
 5. LIGHTING CONTROL DEFAULT SETTING IS TO BE 'TIMER MODE'
 6. EACH LIGHTING CONTROL SYSTEM IS GOVERNED BY THE ILLUMINATOR CONTROL SYSTEM PROVIDING BOTH REMOTE MOBILE CONTROL VIA SMS AND LOCAL CONTROL OPTIONS FOR AUTHORISED USERS.
- MOBILE SMS APPLICATION:
- ACCESSIBLE BY AUTHORISED USERS FOR REMOTE CONTROL OF LIGHTING.
 - USER MANAGEMENT AND NEW/UPDATE OF USERS CAN BE CONFIGURED BY AUTHORISED PERSONNEL.
 - RESTRICTED TO OPERATION DURING NON-CURFEW TIMES, AS DEFINED BY A HIGHER-LEVEL SITE MANAGER AUTHORITY AND COUNCIL.
 - AUTHORISED USERS CAN CONTROL LIGHTING AS PER BELOW:
 - TURN LIGHTS ON OR OFF REMOTELY.
 - RECREATIONAL USE (100%) AND TRAINING (50%)
- MANUAL LIGHTING CONTROL PANEL:
- FITTED WITH MOBILE 4G CONNECTIVITY FOR CONNECTION AND COMMUNICATION TO AUTHORISED USERS VIA SMS.
 - PROVIDES PHYSICAL SWITCHES FOR LIGHTING CONTROL WHEN THE MOBILE APPLICATION OR NETWORK IS UNAVAILABLE.
 - MANUAL OVERRIDE SWITCH ALLOWS BYPASS OF PROGRAMMED LOGIC FOR EMERGENCY OR SPECIAL CONDITIONS.
 - LIGHTING PERFORMANCE SWITCHES ALLOW USERS IN MANUAL OVERRIDE MODE TO CONTROL LIGHTING AS PER BELOW:
 - TURN LIGHTS ON OR OFF REMOTELY.
 - RECREATIONAL USE (100%) AND TRAINING (50%)

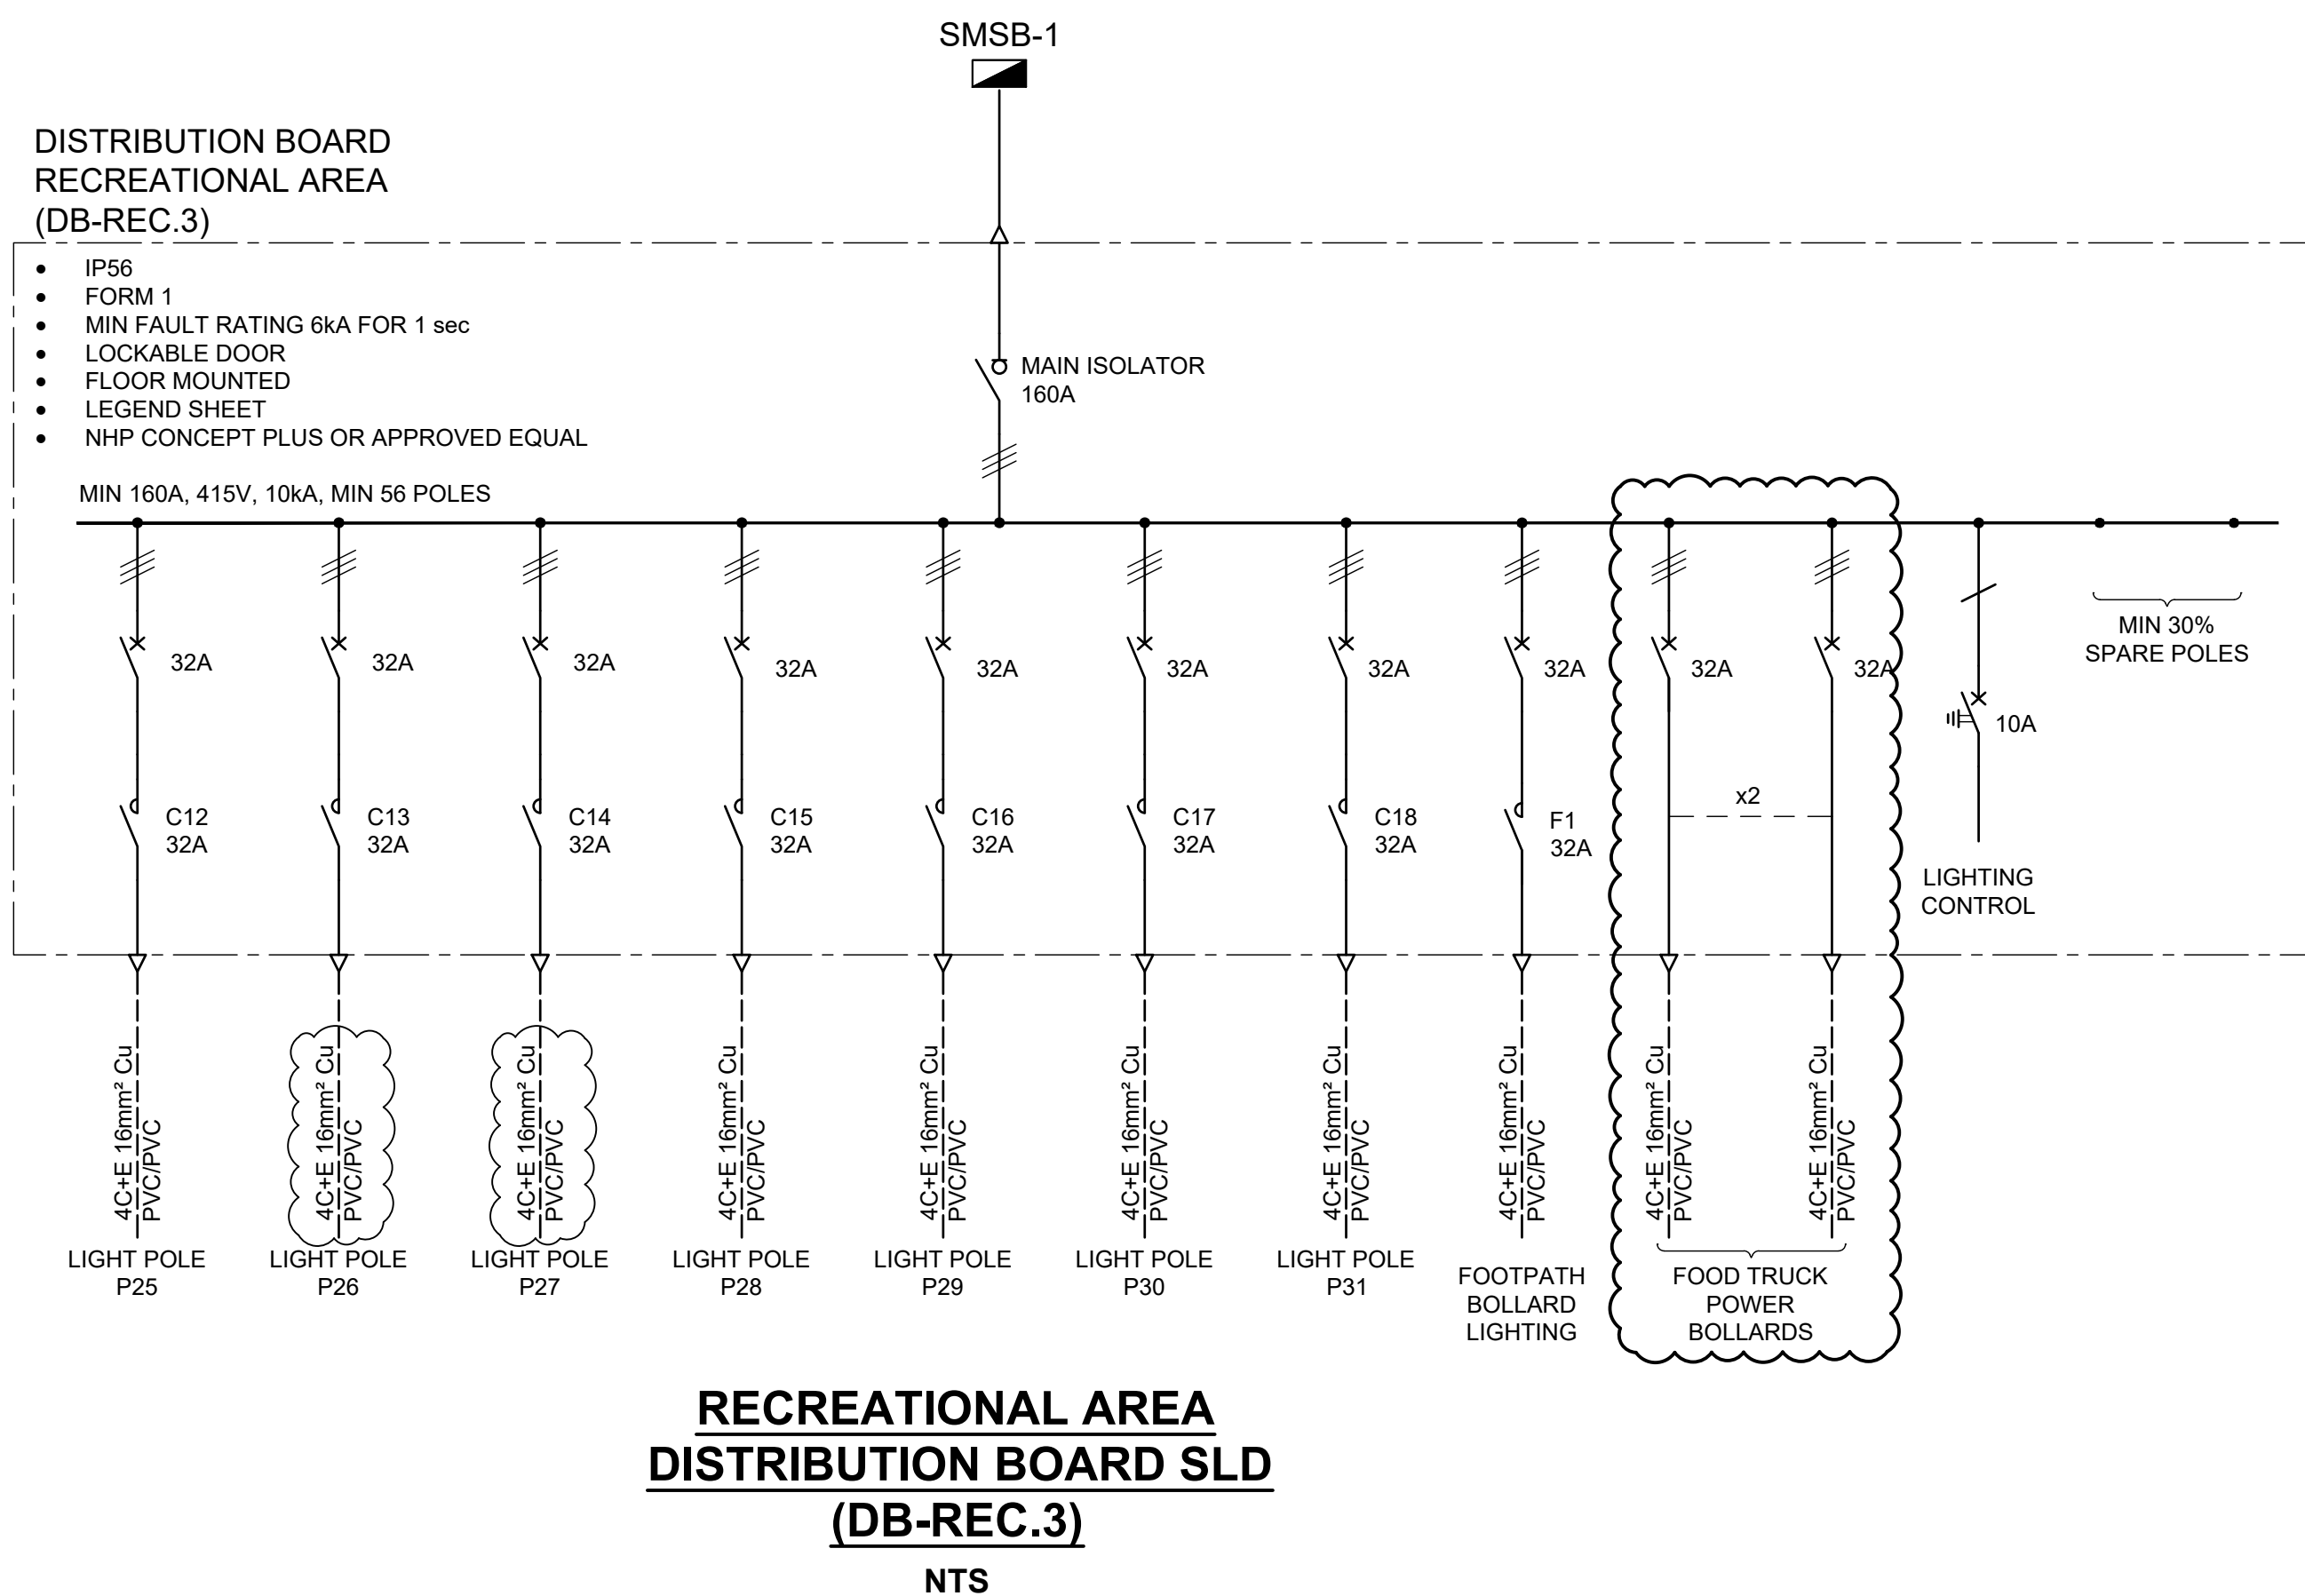

FOR TENDER

ALL DIMENSIONS SHOWN IN MM. DO NOT SCALE FROM DRAWINGS. DIMENSIONS TAKE PRECEDENCE, IF IN DOUBT REFER TO HK SOLUTIONS.										FOR TENDER															
T2	UPDATED ISSUE FOR TENDER					10/07/26	AF	HKS	 ENGINEERING PROJECT MANAGEMENT DARWIN. GEELONG. CAIRNS. TOWNSVILLE. PERTH. BALLARAT admin@hksolutions.com.au www.hksolutions.com.au Conditions of use. This document may only be used by Harris Kmon Solutions clients for the purpose for which it was prepared and must not be used by any other person or for any other purpose.											DRAWN AF		STAGE 1			
T1	ISSUE FOR TENDER					17/06/26	AF	HKS												ROCKHAMPTON NETBALL CENTRE - SITE LAYOUT					
REV.	DESCRIPTION					DATE	INT.	COMPANY												554-700 YAAMBA ROAD, NORMAN GARDEN - 4701					
REVISIONS										RECREATIONAL AREA LIGHTING SLD & SCHEMATICS															
										THIS DRAWING MUST NOT BE USED FOR CONSTRUCTION UNLESS SIGNED AS APPROVED		PAGE No		PROJECT No - DRAWING No		DISCIPLINE		REV.	SHEET SIZE						
												14 OF 16		25015 -E-SITE-306		ELECTRICAL		T2	A1						