


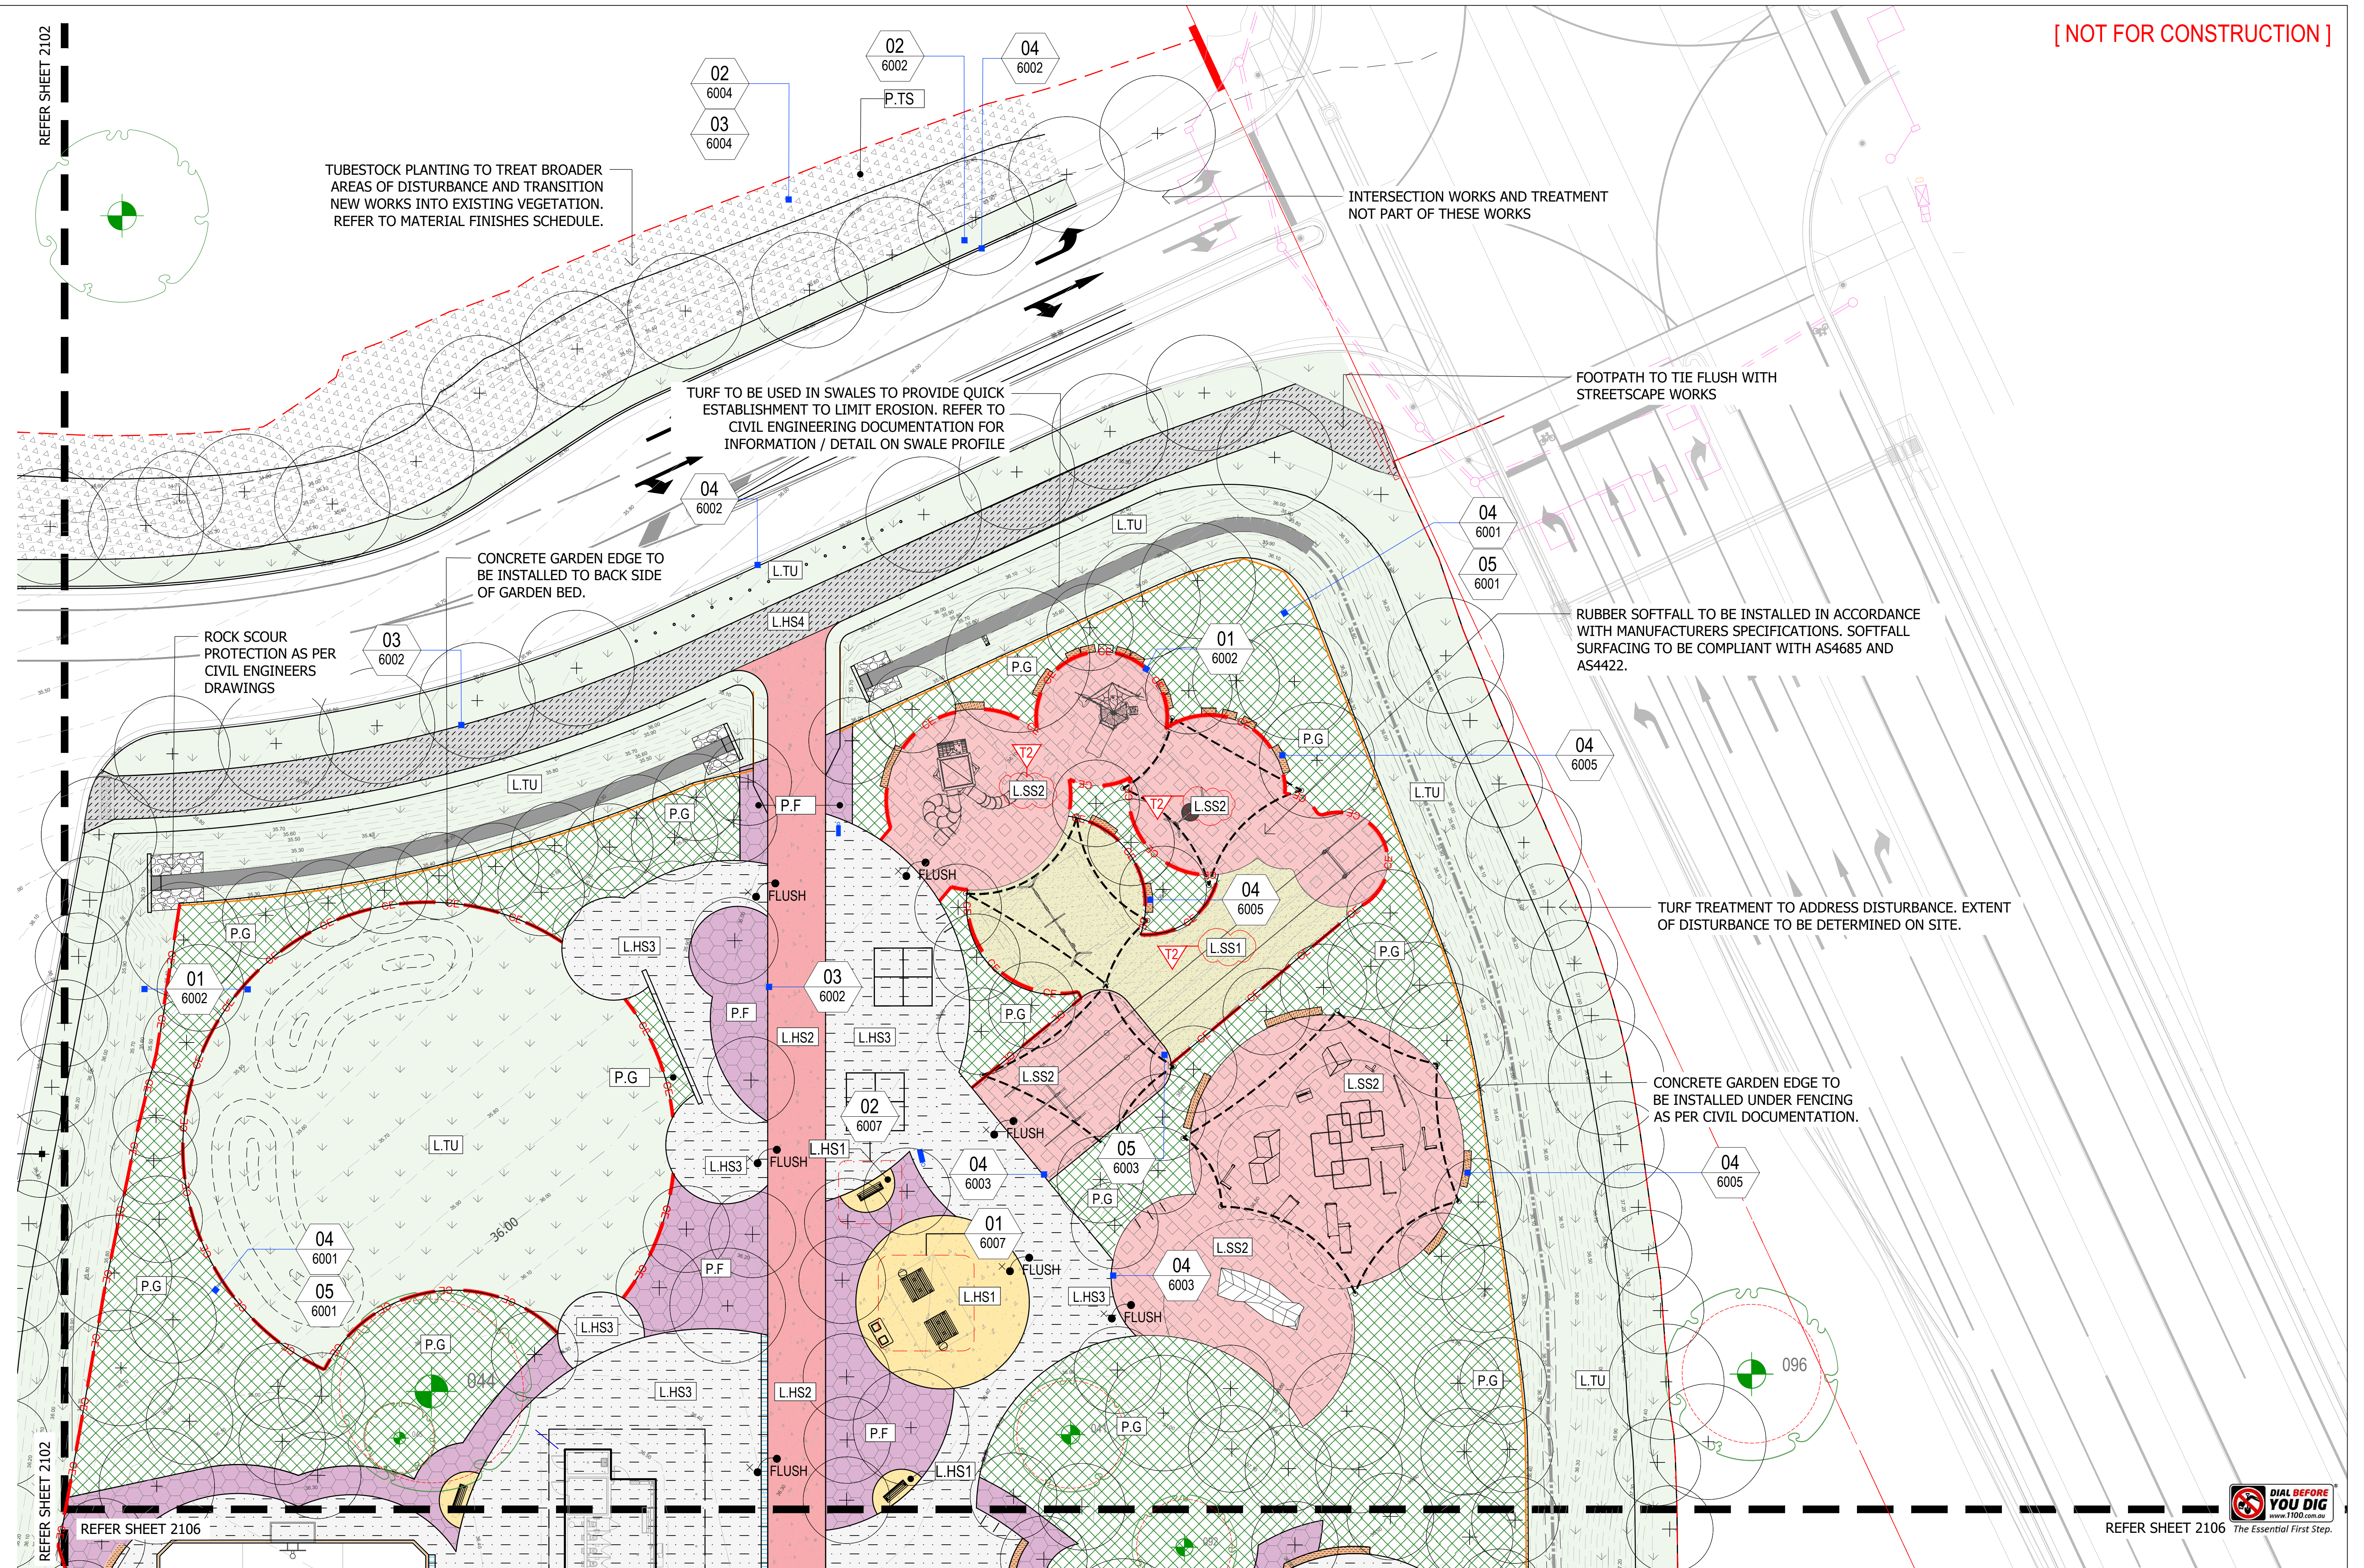

REV	DESCRIPTION	AUTH	CHK	DATE
T1	ISSUE FOR TENDER	CE	AW	18.06.2026
T2	ISSUE FOR TENDER - RESPONSES TO TC011	LM	CE	14.07.2026

- These designs and plans are the copyright of MODE DESIGN Corp. Pty Ltd and cannot be reproduced without written permission.
- Verify all dimensions on site prior to commencement of work. DO NOT scale off these drawings.
- Report any discrepancies to MODE before carrying out any work.
- Where service locations are shown on the drawings they are indicative only. The exact location of existing services is to be confirmed on site by the contractor prior to commencement of work. Dial Before You Dig - Ph 1100. Refer to Service Engineer's drawings for the location of all proposed services.

SCALE
1:200
0m 2 4 6 8 10

NORTH

CLIENT

CONSULTANTS

BRISBANE
Turbal and Yuggara Country
Plaza Level, Mosaic
826 Ann St
Fortitude Valley QLD 4006
T +61 7 3253 9900
bne@modedesign.com.au
ABN: 65 112 807 931

PROJECT
Rockhampton Sports Precinct
Stage 1
544-700 Yaamba Rd, Norman Gardens, QLD
This project is located on Durumbal Land

DRAWING TITLE
SURFACE FINISHES PLAN 03

PROJECT STAGE			
ISSUE FOR TENDER			
MODE PROJECT No	STAGE	DRAWING No	REVISION
24523	IFT	LD-2103	T2