


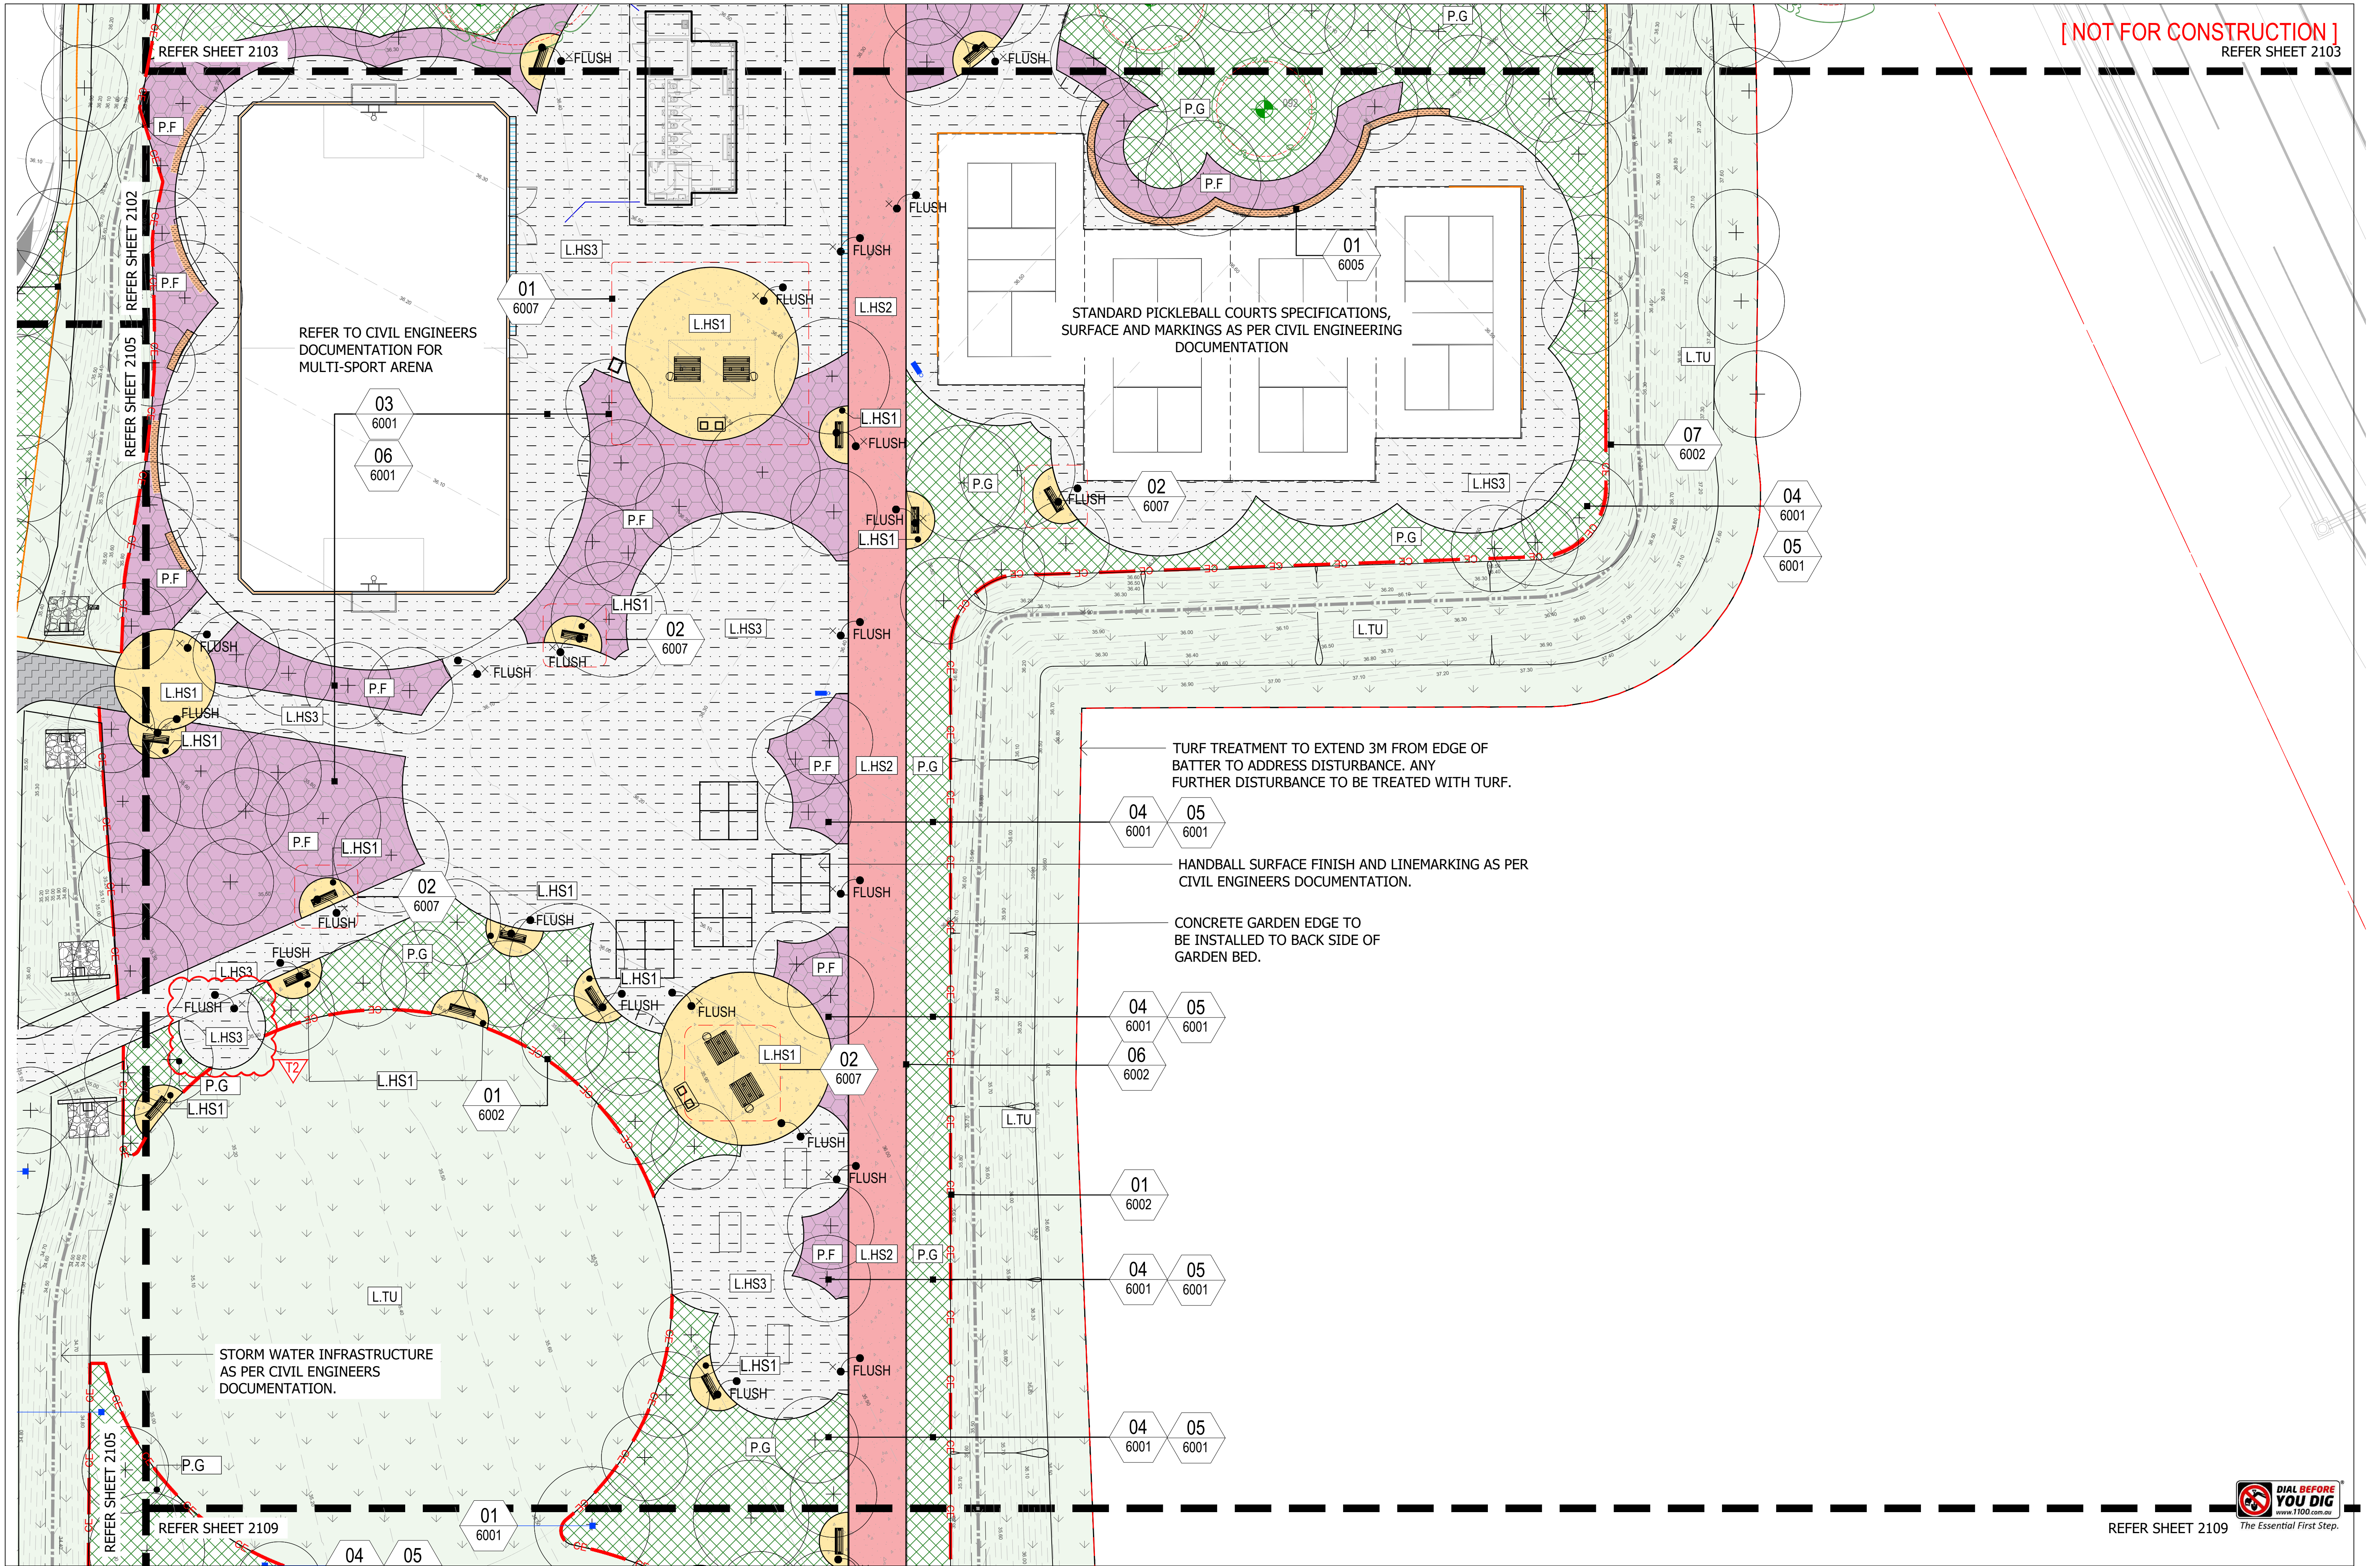

REV	DESCRIPTION	AUTH	CHK	DATE	SCALE	NORTH	CLIENT	CONSULTANTS	PROJECT	DRAWING TITLE	PROJECT STAGE	MODE PROJECT No	STAGE	DRAWING No	REVISION
T1	ISSUE FOR TENDER	CE	AW	18.06.2026	1:200		Rockhampton Regional Council	SPORTENG™ HK Solutions	BRISBANE Turbal and Yuggera Country Plaza Level, Mosaic 826 Ann St Fortitude Valley QLD 4006 T +61 7 3253 9900 bne@modedesign.com.au ABN: 65 112 807 931	Rockhampton Sports Precinct Stage 1	ISSUE FOR TENDER	24523	IFT	LD-2106	T2
T2	ISSUE FOR TENDER - RESPONSES TO TC011	LM	CE	14.07.2026					544-700 Yaamba Rd, Norman Gardens, QLD This project is located on Durumbal Land	SURFACE FINISHES PLAN 06					